




4 8 16

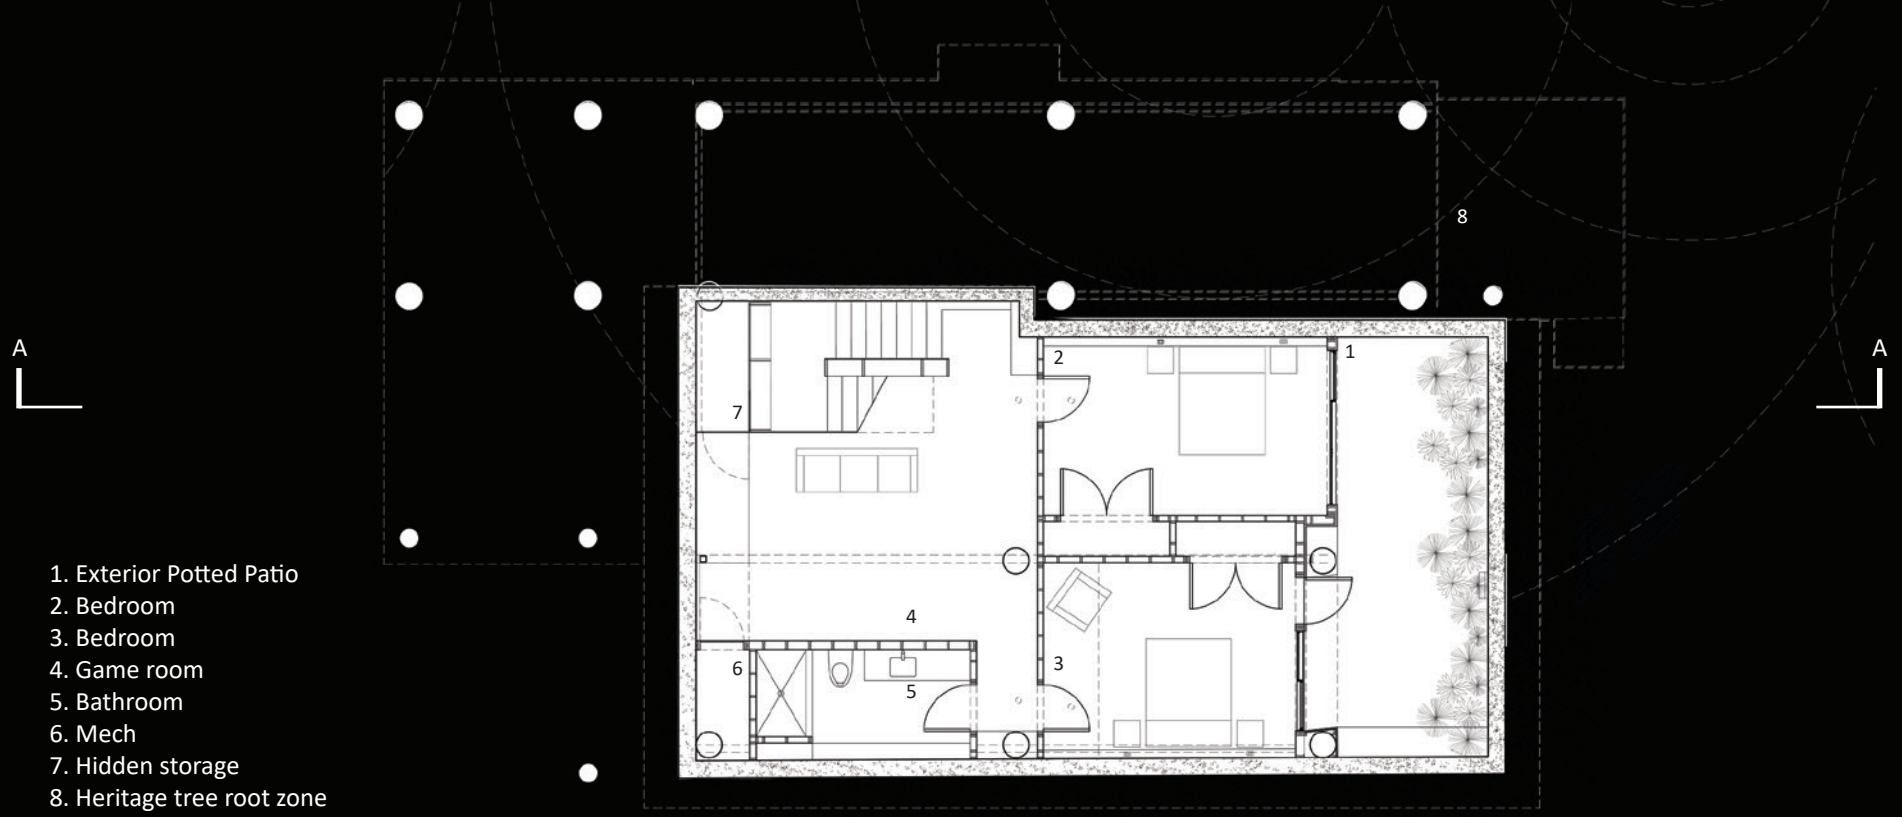

Phase III Basement Plan

The phase I existing piers were 18" diameter concrete that extended at least 10' below grade (some were 15'). **This allowed excavation for the basement without the need to shore up the existing house** and the family could remain during construction.

Phase III Basement Excavation

